
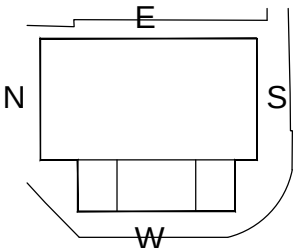


MATERIALS KEY

1. Hardiepanel - Barrique Oak Nature on proprietary carrier system
2. Rainspan Panel
Colour Grey White RAL 9002
3. Insulated through colour resin based render ref. Sto render White RAL 9016. NBS M21.
12. Aluminium 'C' Channel detail between floors 225mm high, flush with Rainscreen face.
21. Powder coated and insulated aluminium capping to top of Hardiepanel rainscreen at top of building.

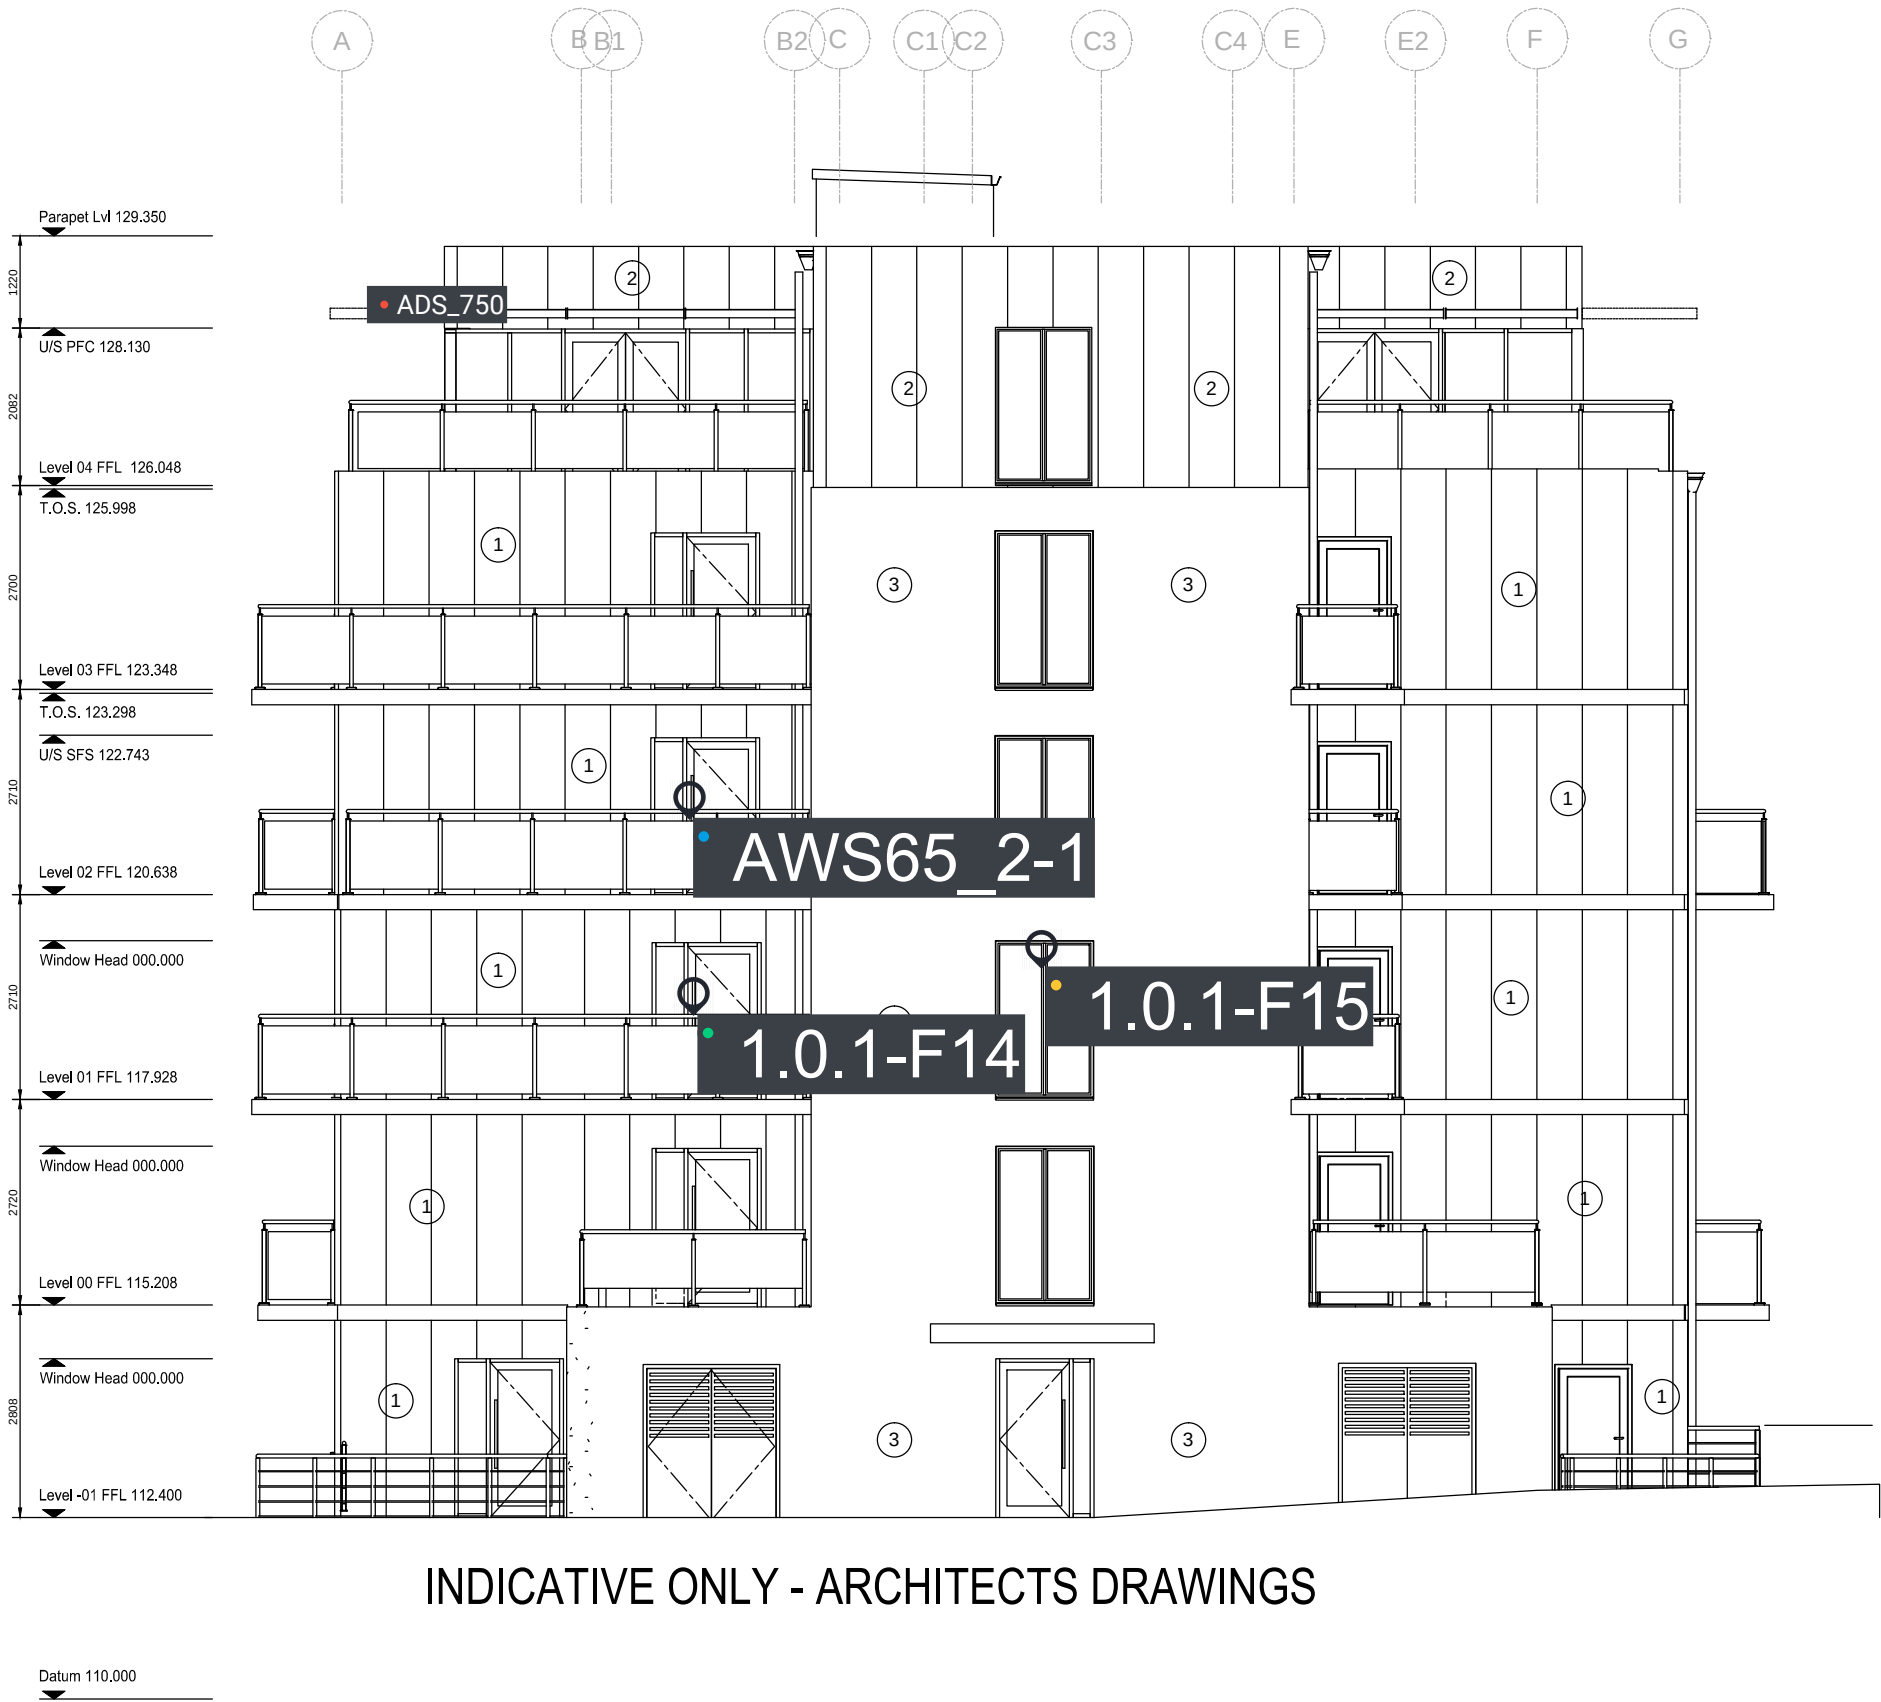

Block Location

West Elevation



The Grove, North Road, South Ockendon, Essex, RM15 6SS. Tel: 01708 858530 - www.sdsamuels.co.uk

Rev	Description	Date
C01	Construction Issue	25.10.21
P02	General Revisions	20.09.21
P01	Preliminary issue	25.08.21

Project:
Gilmartins House, Luton

Client:
MJL Contracts

Title:
West Elevation

Drawing Number:
1736-SDS-XX-ZZ-DR-X-2000

Issue:
CONSTRUCTION

Scale: 1:100 @ A3

Date: July 2021

Contract.
C1746

Rev.
C01

Drawing No.
2000